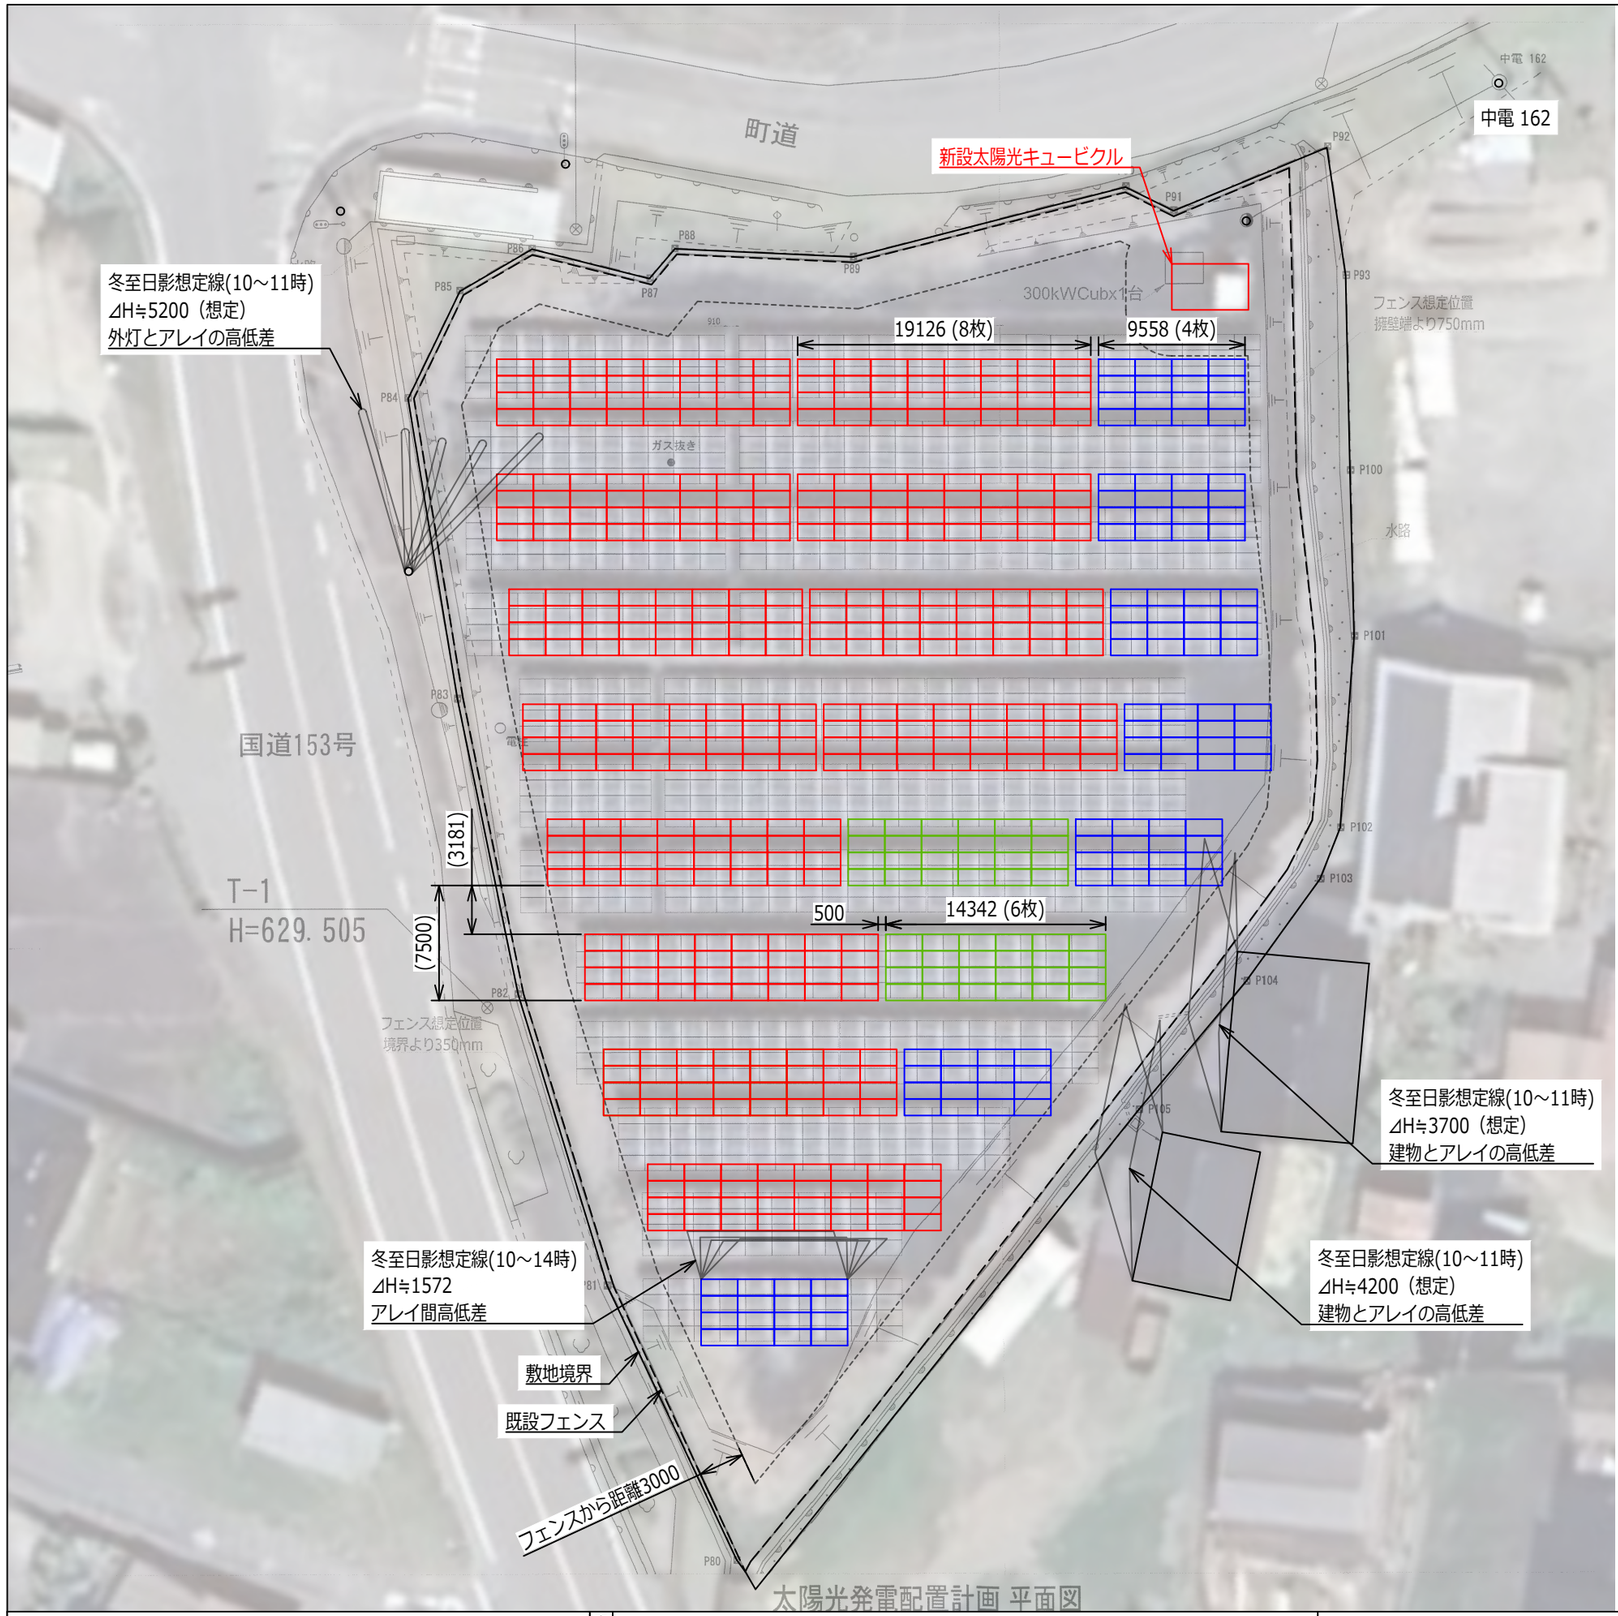

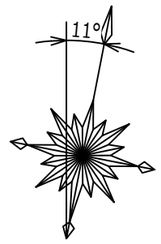

太陽電池モジュール 仕様	
NER132M625E-NGD	
公称最大出力	625 W
公称最大出力動作電圧	41.69 V
公称最大出力動作電流	14.99 A
公称開放電圧	49.19 V
公称短絡電流	16.19 A
質量	32.8 kg
寸法	2382x1134x30
設置場所	地上

PCS 01 (1台)		
SG100CX-JP（三相3線100.0kW）		
モジュール枚数	192 枚	
直列枚数／系統数	16 枚	12 系統
モジュール出力	120.00 kW	
PCS出力	90.00 kW	

PCS 02,03 (2台)		
SG100CX-JP（三相3線100.0kW）		
モジュール枚数	176 枚	
直列枚数／系統数	16 枚	11 系統
モジュール出力	110.00 kW	
PCS出力	90.00 kW	

※ PCS 01～03は90.00kWへ出力制限想定です。

モジュール 合計枚数	544 枚
モジュール総出力	340.00 kW
系統側総出力	270.00 kW

20度傾斜架台_4段8列（32枚）：12基
20度傾斜架台_4段6列（24枚）：02基
20度傾斜架台_4段4列（16枚）：07基

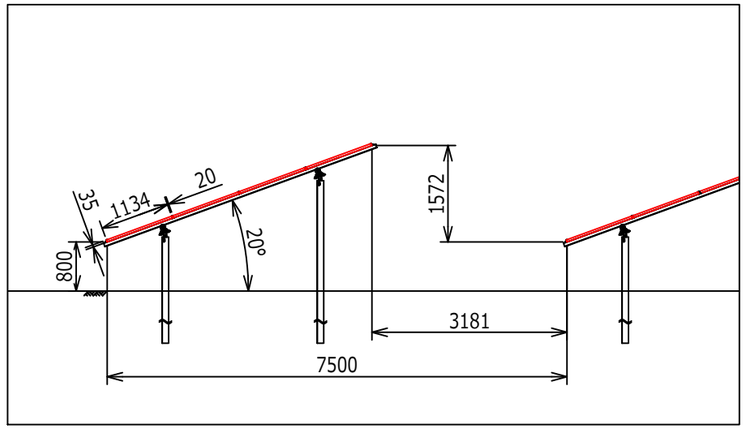

架台参考図(S=1/100)

～ 特記事項 ～
※ 受領資料及び航空写真を基に作成しております。
※ 平坦な土地であり全面に設置できる前提として設計しております。
※ 冬至日影線は実際とは異なる場合がございます。
※ 造成測量後に容量が変更となる場合がございます。
※ 架台詳細仕様につきましては、現地詳細調査後に決定と致します。
※ 本図面は商談用のものであり、設置容量や発電量を保証するものではございません。
※ 機器設置場所の配置は変更となる可能性がございます。

-長野県上伊那郡飯島町-

参考図	案件	トマト第2発電所	明日を未来にする。Next Energy ネクストエナジー・アンド・リソース株式会社	設計	検図	承認	シート	A3	縮尺	1/400
	図名	太陽電池モジュール 配置図		26.01.05 ミン	26.01.05 田村	26.01.05 小泉	RP-0042- SL01-00			